
СТЕЛЛАЖ С ТВ-НИШЕЙ / ПРЕДВАРИТЕЛЬНАЯ СХЕМА


Этап 1 из 3: стеллаж. Дверной блок и стеновые панели в этот лист не входят.

Размеры в мм. Схема новой конструкции по мотивам исходного листа; не является деталировкой для изготовления.

1. Общий вид / М 1:20

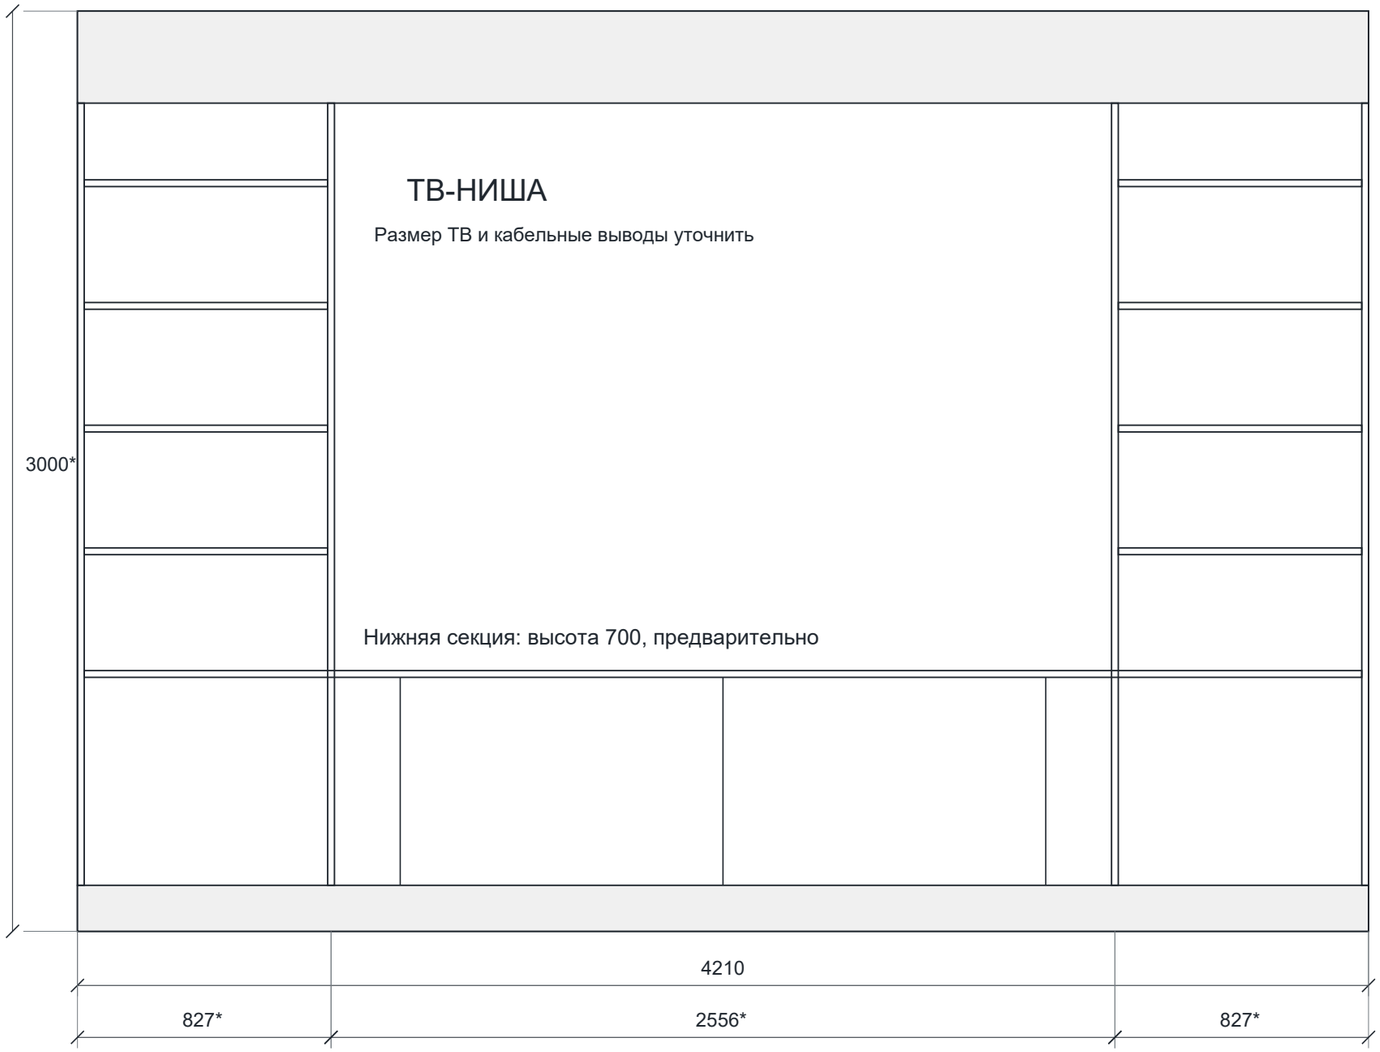

2. Разрез по полке / М 1:20

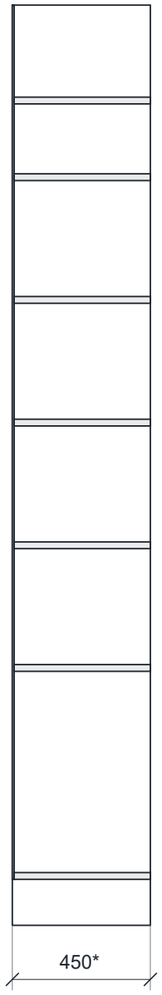


Принятые решения

Корпус и полки: МДФ со шпоном.
Итоговая толщина: 22 мм*.
Задняя стенка: 6 мм*, в паз.
Полки боковых секций: съёмные.
Низ: регулируемые опоры, закрытые съёмным цоколем.
Карниз: отдельный декоративный элемент на монтажной рейке.

* Предварительные значения. Высота 3000 взята как габарит композиции из исходного листа. Рабочую высоту корпуса уточнить по обмеру и профилю карниза.

3. Принцип опирания съёмной полки / без масштаба

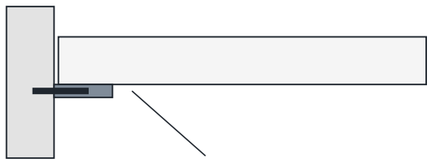

Полкодержатель со штифтом Ø5*

Зазор полки у боковины: 1 мм* с каждой стороны.

Крепёж: 4 опоры на полку, с фиксацией от сдвига.

Модель опоры, присадку и нагрузку уточнить до выпуска деталей.

Стационарные связи: мебельные стяжки и шканты, тип уточнить.

Перед деталировкой

1. Проверить размеры помещения.
2. Согласовать толщину со шпоном.
3. Уточнить ТВ и нагрузку полок.
4. Выбрать конкретную фурнитуру.
5. Проработать крепление к стене по материалу основания.

СТАДИЯ: ЭСКИЗ / Лист 1 из 1

Дата: 16.10.2026

Исходник: redirect.pdf, лист 1